
[공개]


7

4. 도 면

자격종목	컴퓨터응용선반기능사	과제명	선반가공작업	척도	N S

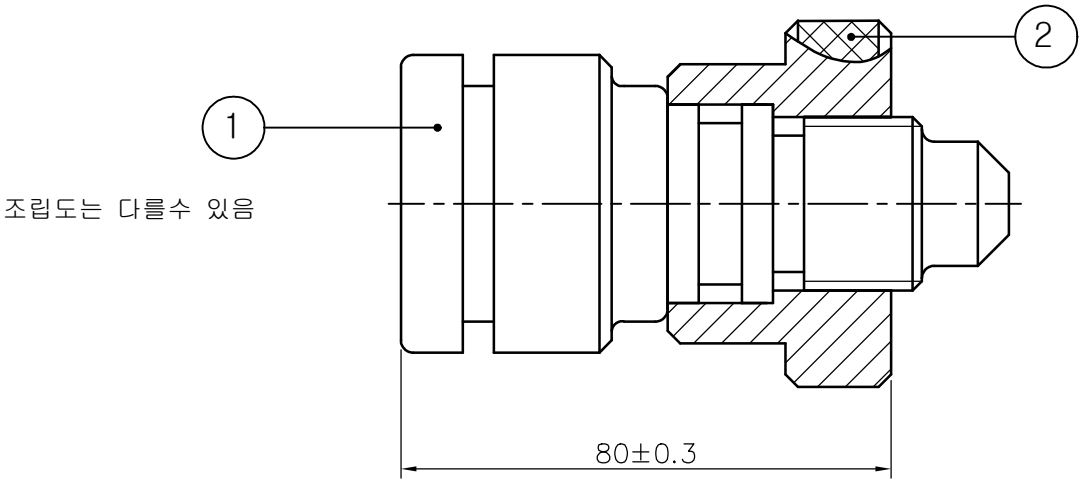

조립도는 다를수 있음

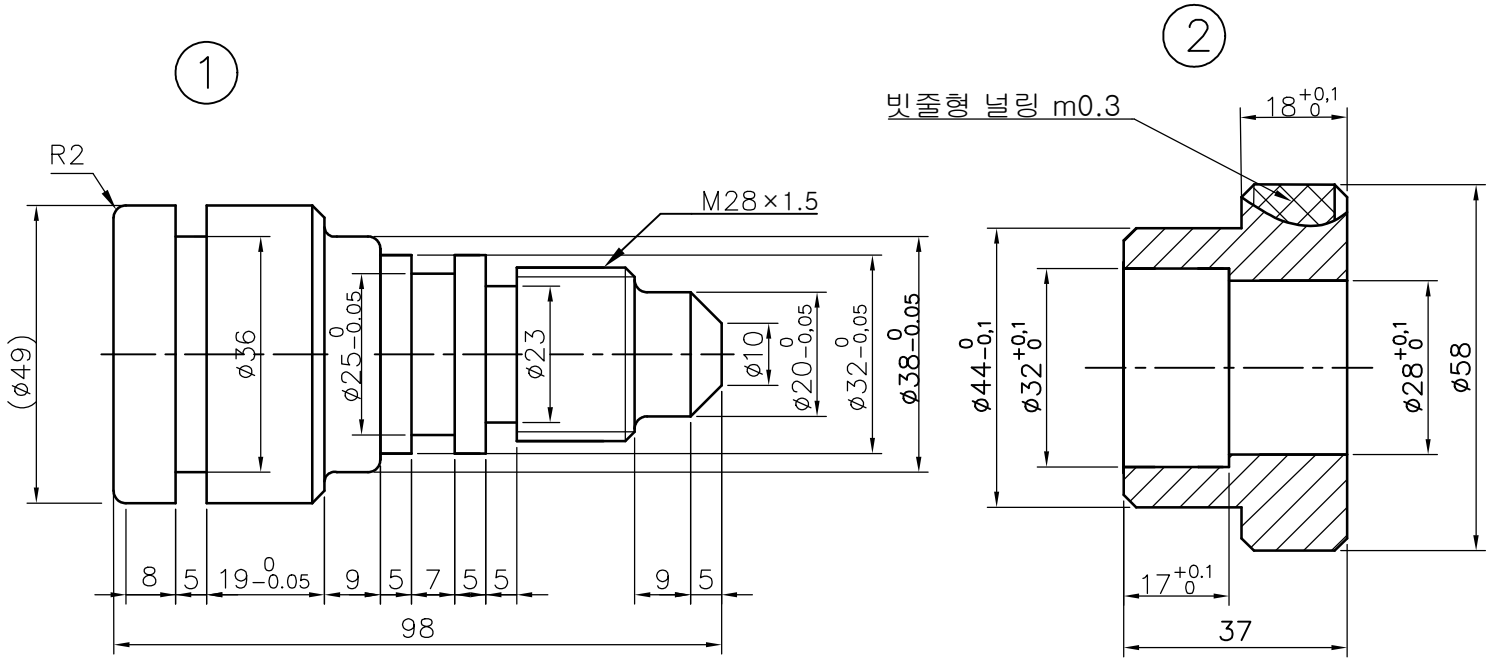

주 서

1. 도시되고 지시되지 않은 라운드 R2
2. 도시되고 지시없는 모따기 C2

구분 \ 공차		M28 x 1.5 - 보통급
수나사	외 경	27.968 0 -0.236
	유효경	26.994 0 -0.150