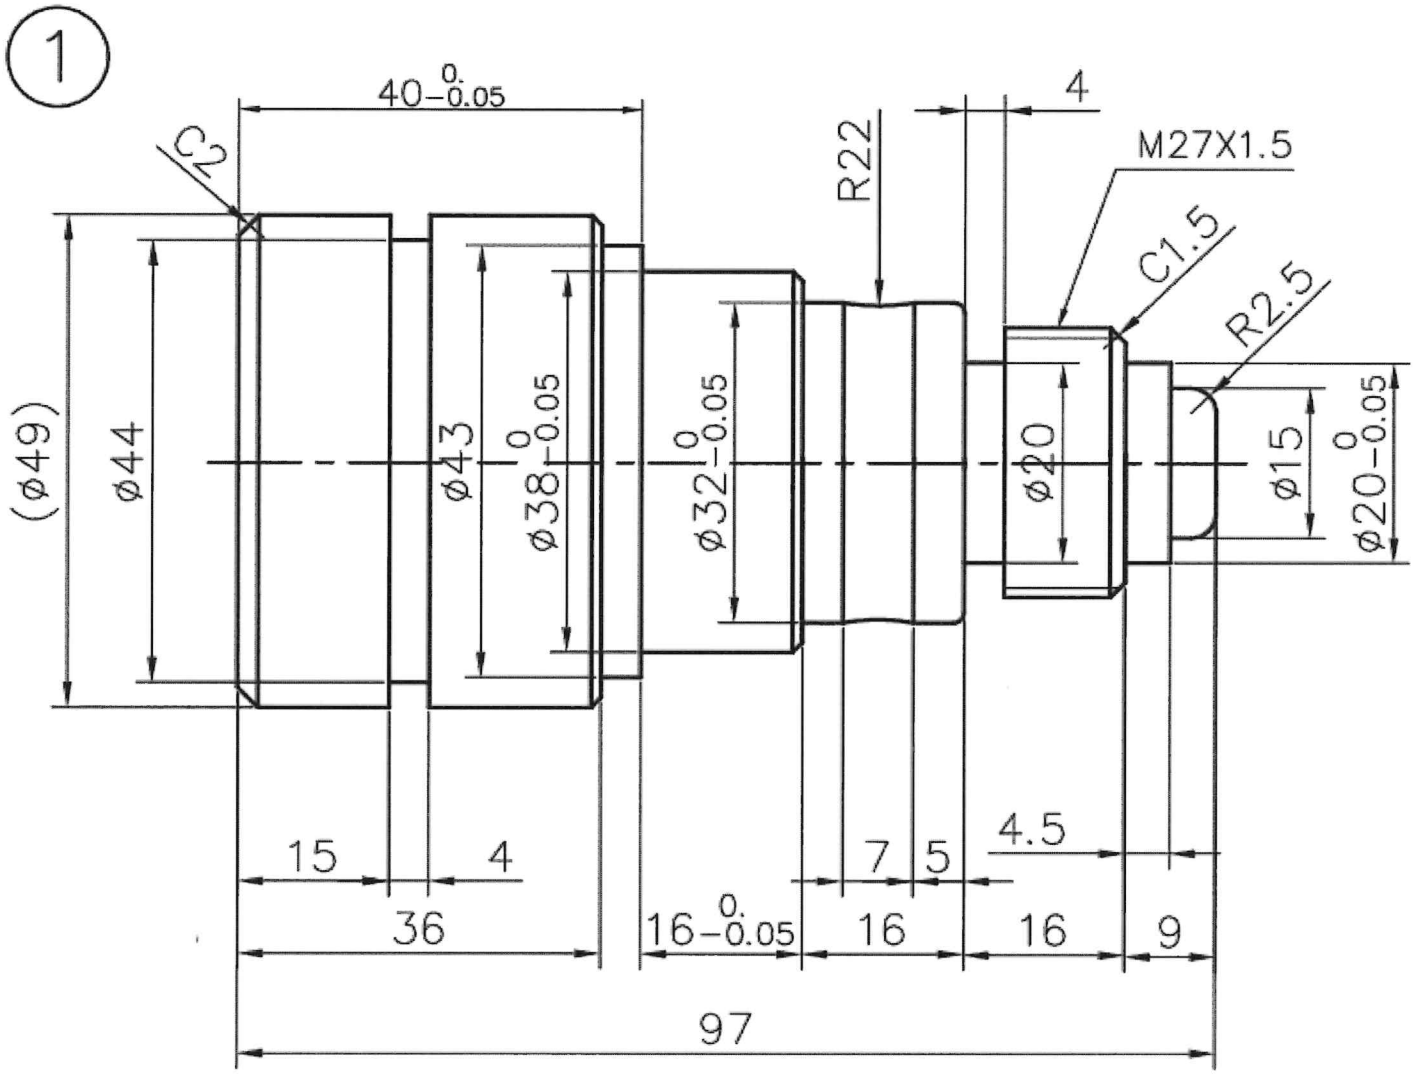


주 서

1. 도시되고 지시없는 라운드 R1
2. 도시되고 지시없는 모따기 C1

13번 뒷단	
1	
2	
홈가공	
1	G00 X54. Z-
2	G75 X Z-
앞단	
1	
2	
3	
4	
5	
6	
7	
8	
9	
10	
11	
12	
13	
14	
15	
16	
17	
18	
홈가공	
1	G00 X Z-
2	G75 X Z-
나사가공	
1	G00 X Z-
2	G76 X Z- P890 Q350 F1.5